
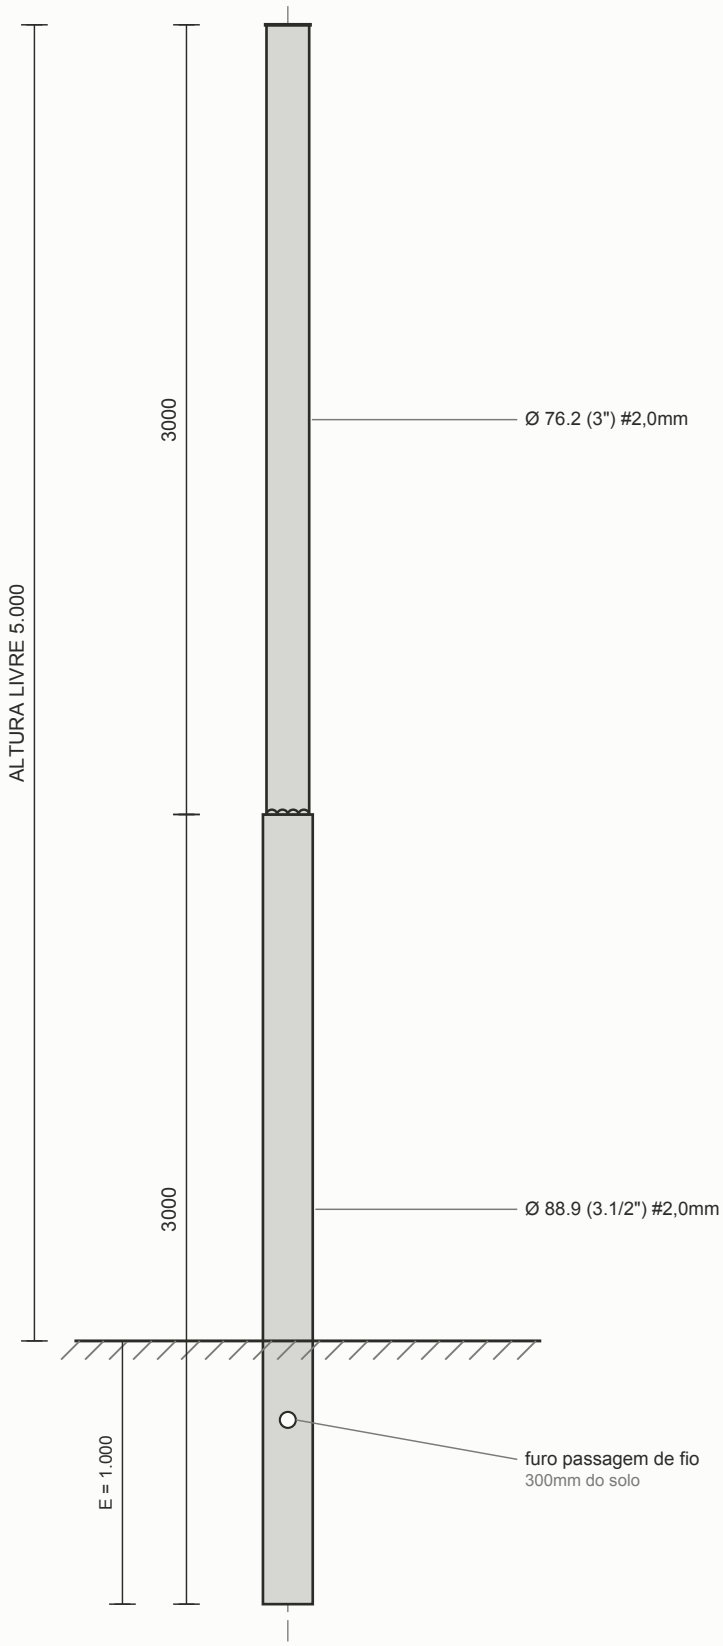


VISTA LATERAL — ENGASTADO

medidas em mm

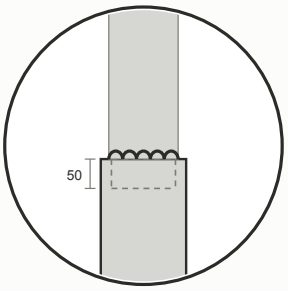

EMENDA FIXA

encaixe de 50mm soldado
solda circunferencial estrutural

DIFERENCIAIS DE FABRICAÇÃO

CORTE A LASER
precisão sem quinas vivas

SEM REBARBAS
acabamento limpo e seguro

SOLDA MIG
união estrutural de alta resistência

B&B ILUMINAÇÃO

POSTE TELECÔNICO RETO URBAN PRO

ALTURA LIVRE 5,0 m · ENGASTADO · 30 daN

MATERIAL: Aço SAE 1010/1020 · paredes por seção (mapa 05/08)
ACABAMENTO: Galvanizado a fogo (NBR 6323)
CARGA NOMINAL: 30 daN no topo · ruptura 60 daN · NBR 14744
PESO: 24 kg · E = 1000 mm · FLECHA 134/200 mm

BB-URB-PRO-TR05-E
CÓDIGO DO PRODUTO

DATA
04/11/2026