
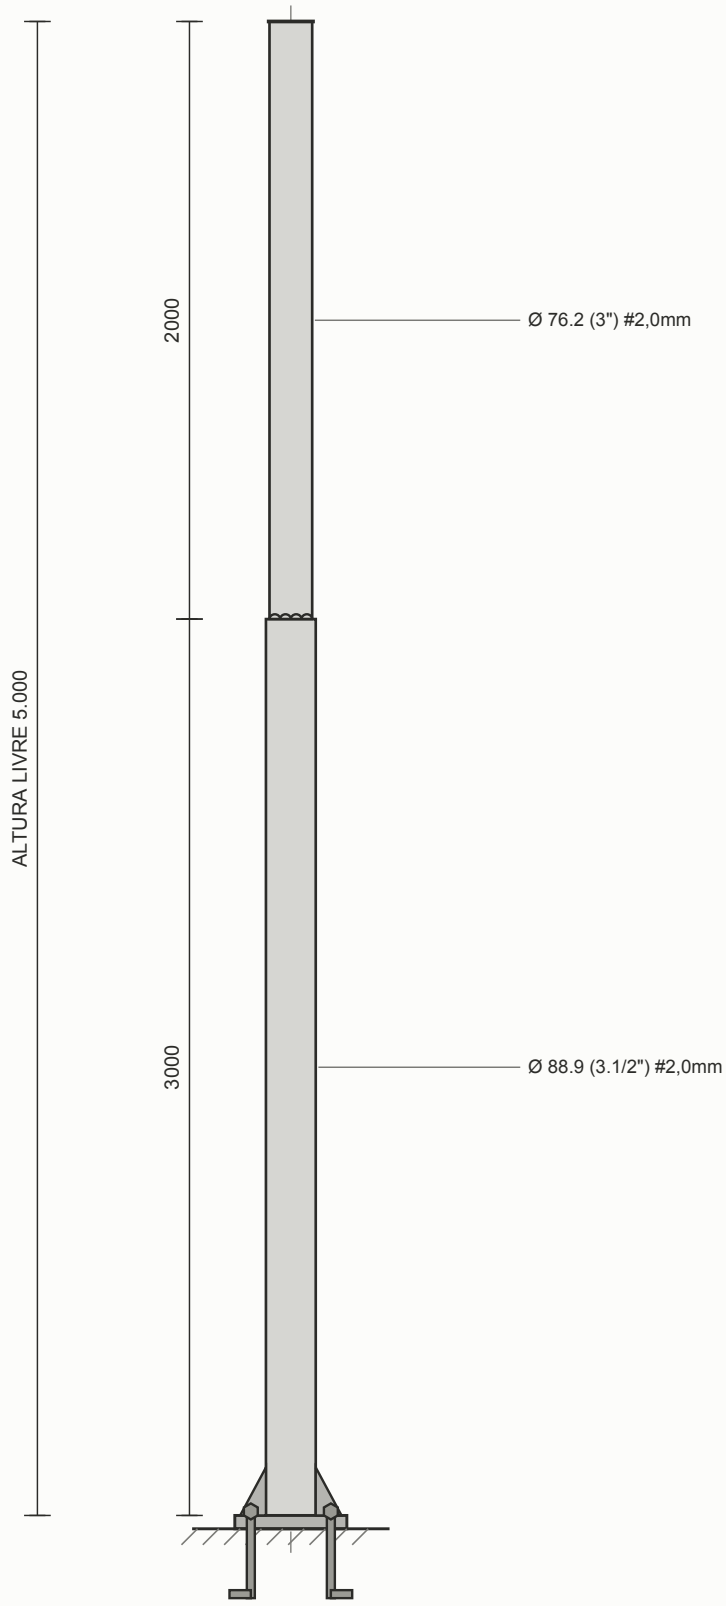



VISTA LATERAL — FLANGEADO

medidas em mm

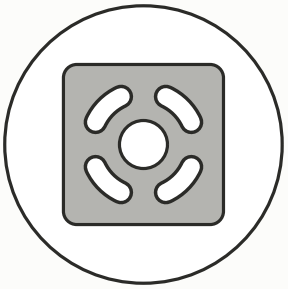

SAPATA / FLANGE

placa 200×200mm · chapa 3/8"
furos oblongos em curva — nivelamento

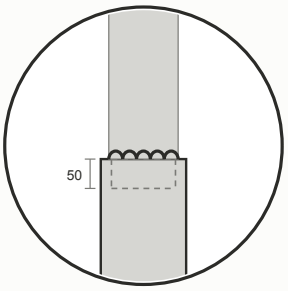

EMENDA FIXA

encaixe de 50mm soldado
solda circunferencial estrutural

DIFERENCIAIS DE FABRICAÇÃO

CORTE A LASER
precisão sem quinas vivas

SEM REBARBAS
acabamento limpo e seguro

SOLDA MIG
união estrutural de alta resistência

B&B ILUMINAÇÃO

POSTE TELECÔNICO RETO URBAN PRO

ALTURA LIVRE 5,0 m · FLANGEADO · 30 daN

MATERIAL: Aço SAE 1010/1020 · paredes por seção (mapa 05/08)
ACABAMENTO: Galvanizado a fogo (NBR 6323)
CARGA NOMINAL: 30 daN no topo · ruptura 60 daN · NBR 14744
PESO: 23 kg (c/ sapata) · SAPATA 200x200 3/8" · FLECHA 123/200 mm

BB-URB-PRO-TR05-F
CÓDIGO DO PRODUTO

DATA
04/11/2026